


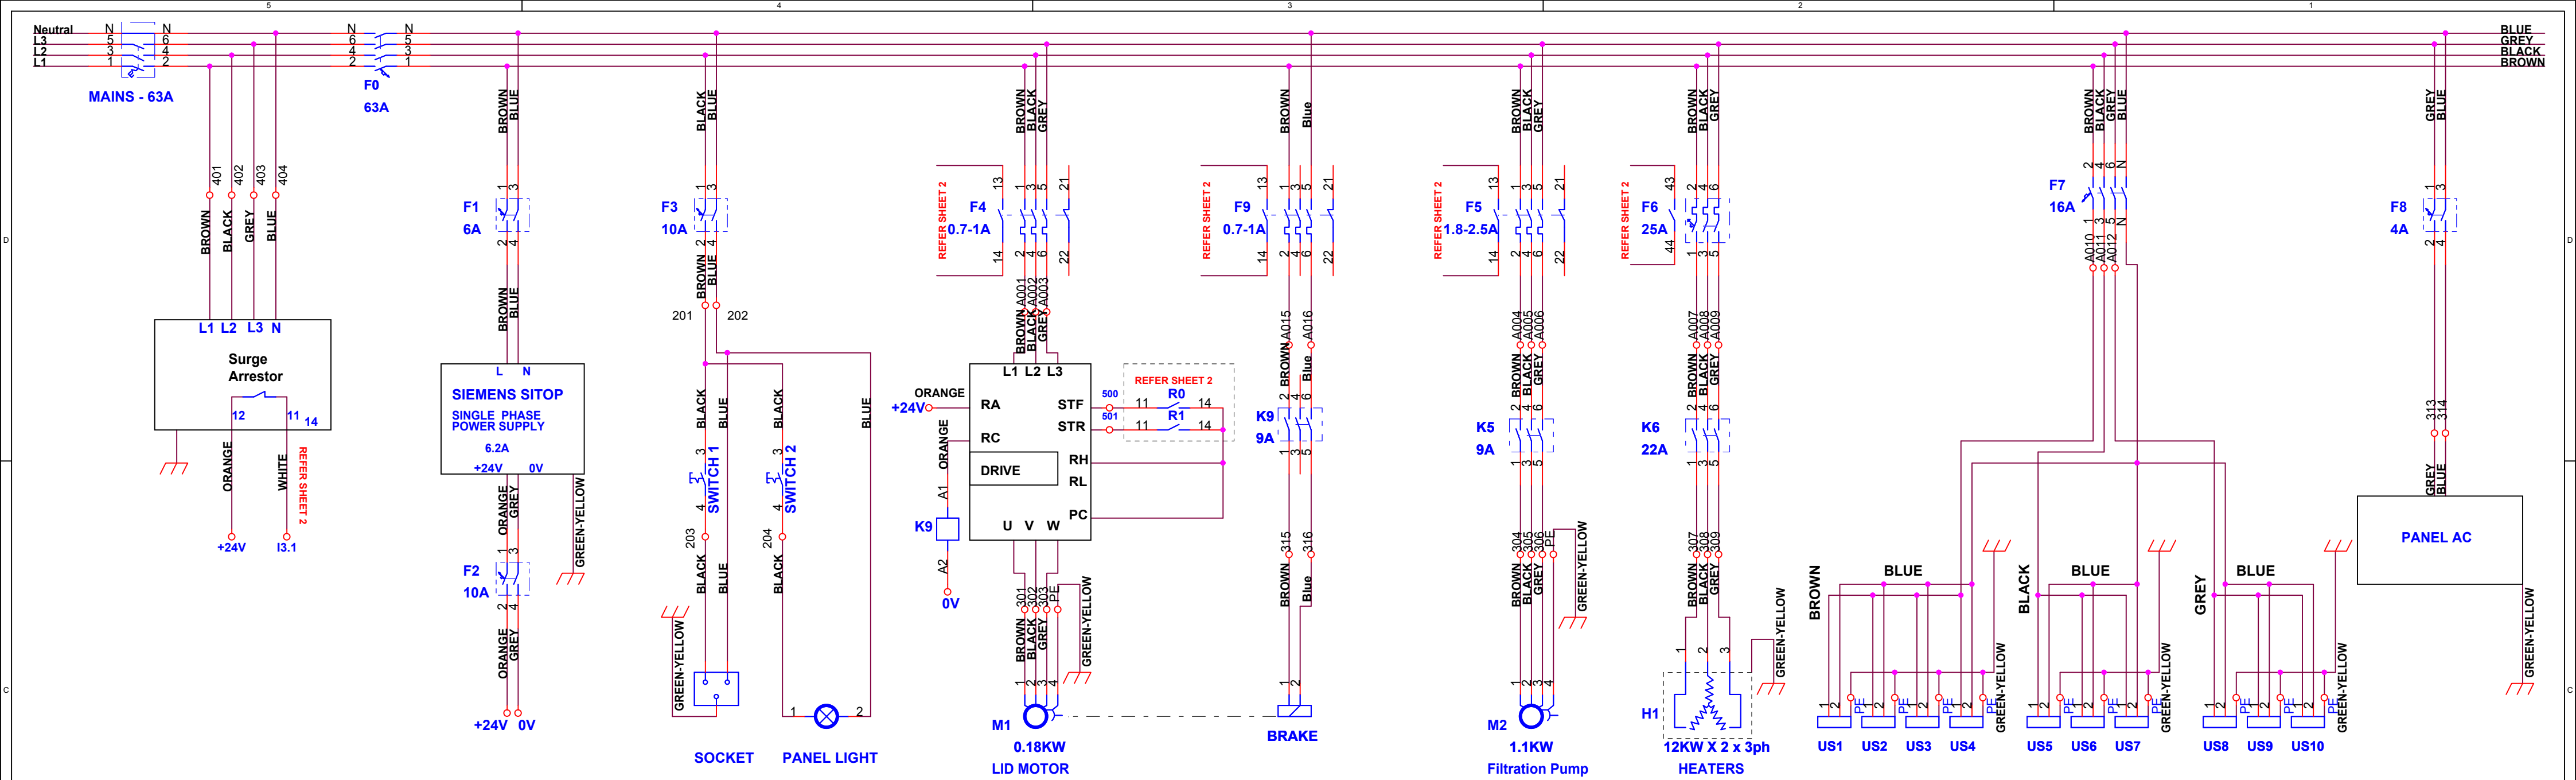

NOTE: SURGE SUPPRESSOR TO BE CONNECTED WITH ALL CONTACTORS.

Total Load = 39KW (Approx)

Total Current = 56Amp (Approx)

